- THESE PLANS SHALL BE READ IN CONJUNCTION WITH ANY STRUCTURAL OR CIVIL ENGINEERING COMPUTATIONS & DRAWINGS. DO NOT SCALE DRAWINGS. WRITTEN DIMENSIONS TAKE PRECEDENCE OVER SCALE.

- THE OWNER/BUILDER, SUBCONTRACTOR SHALL VERIFY ALL DIMENSIONS, LEVELS, SETBACKS & SPECIFICATIONS PRIOR TO COMMENCING ANY WORKS OR ORDERING MATERIALS & SHALL BE RESPONSIBLE FOR ENSURING THAT ALL BUILDING WORKS CONFORM TO THE NATIONAL CONSTRUCTION CODE, AS CODES (CURRENT EDITIONS) BUILDING REGULATIONS, LOCAL BY-LAWS, & TOWN PLANNING REQUIREMENTS. REPORT ALL DISCREPANCIES TO BUILDING DESIGNER FOR CLARIFICATION.

- THIS DOCUMENTATION HAS BEEN PREPARED FOR THE EXCLUSIVE USE OF THE CUSTOMER. ANY OTHER PERSON WHO USES OR RELIES ON THESE PLANS WITHOUT THE DESIGNERS WRITTEN CONSENT DOES SO AT THEIR OWN RISK & NO RESPONSIBILITY IS ACCEPTED BY THE BUILDING DESIGNER FOR SUCH USE AND/OR RELIANCE.

- THESE NOTES ARE NEITHER EXHAUSTIVE NOR A SUBSTITUTE FOR REGULATIONS, STATUTORY REQUIREMENTS, BUILDING PRACTICE OR CONTRACTUAL OBLIGATIONS & UNLESS EXPRESSLY STATED OTHERWISE, ARE PROVIDED ONLY AS GUIDELINES.

- SAFETY GLAZING TO BE USED IN THE FOLLOWING CASES:
  - i) ALL ROOMS - WITHIN 500mm VERTICAL OF THE FLOOR
  - ii) BATHROOMS - WITHIN 2000mm VERTICAL FROM THE BATH BASE
  - iii) LAUNDRY - WITHIN 1200mm VERTICAL FROM FLOOR AND/OR WITHIN 300mm HORIZONTAL FROM DOORS
  - iv) DOORWAY - WITHIN 300mm HORIZONTAL FROM ALL DOORS
  SHOWER SCREENS SHALL BE GRADE A SAFETY GLASS

  ALL GLAZING THICKNESS TO BE DETERMINED FROM THE APPROPRIATE WIND TERRAIN CATEGORY ABOVE NOT APPLICABLE.

- MAXIMUM AREA OF CLEAR PATTERNED GRADE 'A' SAFETY GLASS MATERIAL FOR FRAMED GLASS, FRAMED GLASS SIDE PANELS AND OTHER GLAZED PANELS AS PER A.S.1288-2006.

TOUGHENED SAFETY GLASS		LAMINATED SAFETY GLASS	
THICKNESS(mm)	AREA(mm)	THICKNESS(mm)	AREA(mm)
3	1.0	5.38	2
4	2.0	6.38	3
5	3.0	8.38	5
6	4.0	10.38	7
8	6.0	12.38	9
10	8.0		
12	10.0		

- WHERE THE BUILDING (OTHER THAN A CLASS 10a) IS LOCATED IN A DESIGNATED TERMITE INFESTATION AREA THE BUILDING SHALL BE PROTECTED IN ACCORDANCE WITH THE RELEVANT AUSTRALIAN STANDARD (A.S. 3660).

- MINIMUM 20% PERMEABILITY AS PER REGULATION 412

- WINDOW SIZES ARE NOMINAL ONLY. ACTUAL SIZE WILL VARY ACCORDING TO MANUFACTURER. WINDOWS TO BE FLASHED ALL AROUND.

- ALL WET AREAS TO COMPLY WITH BCA F1.7 OR AS 3740-2010. WALL FINISHES SHALL BE IMPERVIOUS TO A HEIGHT OF 1800mm ABOVE FLOOR LEVEL TO SHOWER ENCLOSURES & 150mm ABOVE BATHS, BASINS, SINKS & TROUGHS IF WITHIN 75mm OF THE WALL.

- SUB-FLOOR VENTS TO PROVIDE A RATE OF 7500mm sq CLEAR VENTILATION PER 1000mm RUN OF EXTERNAL MASONRY WALL & 22000mm sq CLEAR VENTILATION PER 1000mm RUN OF INTERNAL DWARF WALLS.

- ALL WORKS SHALL COMPLY WITH BUT NOT BE LIMITED TO THE FOLLOWING AUSTRALIAN STANDARDS:-
  - A.S. 1288-2006 GLASS IN BUILDINGS - SELECTION & INSTALLATION
  - A.S. 1562.2-1999 DESIGN & INSTALLATION OF SHEET ROOF & WALL CLADDING. CORRUGATED FIBRE-REINFORCED CEMENT
  - A.S. 1684-2010 RESIDENTIAL TIMBER FRAMED CONSTRUCTION. PART 1,2,3,4
  - A.S. 2047-2014/ AMDT 2-2001 WINDOWS IN BUILDINGS-SELECTION & INSTALLATION
  - A.S. 2049-2002/AMDT 1-2005 ROOF TILES
  - A.S. 2050-2002/AMDT 1-2005 INSTALLATION OF ROOFING TILES
  - A.S. 2870-2011/AMDT 4-2003 RESIDENTIAL SLABS & FOOTINGS- CONSTRUCTION
  - A.S. 2904-1995/AMDT 1-1998 DAMP-PROOF COURSES & FLASHINGS
  - A.S. 3600-2009 CONCRETE STRUCTURES
  - A.S. 3660.1-2000 TERMITE MANAGEMENT-NEW BUILDING WORK
  - A.S. 3700 SUPP. 1-2004 MASONRY STRUCTURES
  - A.S. 3740-2010 WATERPROOFING OF WET AREAS WITHIN RESIDENTIAL BUILDINGS
  - A.S. 3786-1993/AMDT 4-2004 SMOKE ALARMS
  - A.S. 4100 SUPP. 1-1998 STEEL STRUCTURES
  - A.S. 4256-2006 PLASTIC ROOF & WALL CLADDING MATERIALS. PART 1-3 1994 AND PART S 1996
  - A.S. 4773.2-2010 MASONRY IN SMALL BUILDINGS

- FOR INSULATION REQUIREMENTS REFER TO RELEVANT ENERGY RATERS REPORT AND DATA.

- PROVIDE WALL TIES TO BRICKWORK @ MAX. 600mm CRS IN EACH DIRECTION & WITHIN 300mm OF ARTICULATION JOINTS

- SELF SEALING EXHAUST FANS WITH MINIMUM AIR EXCHANGE RATE OF 25LT/SEC TO BE INSTALLED AS REQUIRED.

- SMOKE ALARMS TO BE PROVIDED & INSTALLED IN ACCORDANCE WITH AS 3786-1993 & UNLESS INSTALLED IN AN EXISTING PART OF A CLASS 1,2 OR 3 BUILDING OR A CLASS 4 PART OF A BUILDING THE SMOKE ALARM SHALL BE HARD WIRED WITH BATTERY BACK-UP. ALL ALARMS MUST BE INTERCONNECTED.

- CHIMNEY OR OPEN SOLID FUEL HEATERS ARE TO BE PROVIDED WITH DAMPER OR FLAP.

- ALL CONCRETE & CONCRETE PRACTICE IS TO BE IN ACCORDANCE WITH STANDARDS ASSOCIATION OF AUSTRALIA-1480.

CERTIFIED
BUILDING SURVEYING
Building Permit
Building Act 1993
(Building Regulations 2018)
Ice Konjarski
(BS-L39384)
Date: 19 Aug 2019
BP: 761415120622870
INSPECTION BOOKINGS
9374 4883
24HRS NOTICE REQUIRED

- STAIR REQUIREMENTS:- (OTHER THAN SPIRAL STAIRS)
  - RISERS - 190mm MAX, 115mm MIN.
  - TREADS - 355mm MAX, 240mm MIN. (PRIVATE STAIRS & 250mm PUBLIC STAIRS)
  - RISERS & TREADS TO BE CONSTANT IN SIZE THROUGHOUT FLIGHT.
  - ALL TREADS MUST HAVE, A SURFACE WITH A NON-SLIP CLASSIFICATION OR A NOSING STRIP WITH A NON-SLIP CLASSIFICATION AS PER TABLE 3.9.1.1 OF THE NCC BCA 2015 - (APPLIES TO EXTERNAL STEPS AS WELL).
  - PROVIDE NON-SLIP FINISH OR SUITABLE NON-SKID STRIP NEAR EDGE OF NOSING.
  - ENSURE MAXIMUM GAP BETWEEN RISERS DOES NOT EXCEED 125mm OR USE CLOSED RISERS.
  - PROVIDE CONTINUOUS HANDRAIL 1000mm MIN. HEIGHT TO BALCONIES & DECKS WHICH ARE 1000mm OR MORE ABOVE GROUND LEVEL
  - 865mm MIN. HEIGHT CONTINUOUS HANDRAIL ABOVE STAIR NOSING & LANDINGS
  - MAX. OPENINGS BETWEEN BALUSTERS NOT TO EXCEED 125mm.
  - A SINGLE FLIGHT OF STAIRS SHALL NOT HAVE MORE THAN 18 OR LESS THAN 2 RISERS

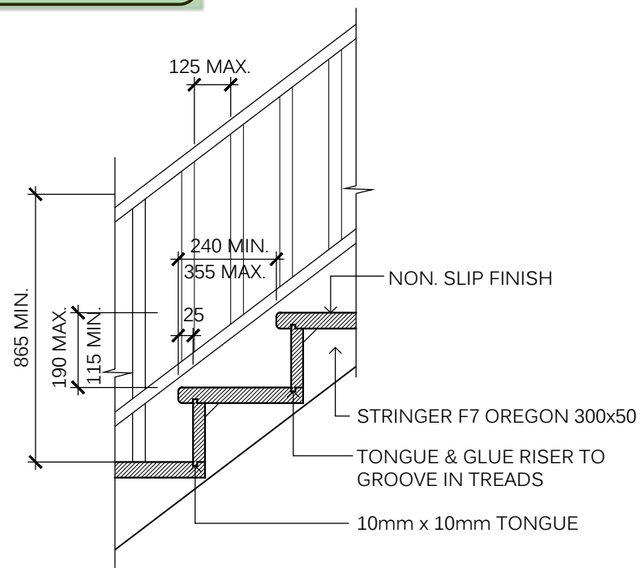

- TIMBER CONSTRUCTION IS TO CONFORM TO THE REQUIREMENTS OF AS 1684 & AS 1720.
  ALL TIMBER SPECIFIED ON THE DRAWINGS IS TO HAVE THE FOLLOWING MINIMUM STRESS GRADE UNLESS OTHERWISE NOTED:-

UNSEASONED HARDWOOD	F8
SEASONED or KILN DRIED HARDWOOD	F17
LAMINATED PINE	F8
RADIATA PINE	F5
OREGON	F7

DEVELOPMENT SCHEDULE

SITE AREA:	696.64m²
BUILDING AREA:	324.31m²
SITE COVERAGE:	46.00%.
O/A BUILDING HT:	6.657m
MELWAYS REF:	26 G6
MUNICIPALITY:	BRIMBANK

JOB ADDRESS

PROPOSED:	MULTI-UNIT DEVEL.
AT:	28 ROMSEY AVE, NTH SUNSHINE VIC 3020
FOR:	URAS ENTERPRISES
DATE:	13/06/2019
SHEET No:	01 OF 14
JOB No:	14 040

THESE PLANS SHALL BE READ IN CONJUNCTION WITH THE RELEVANT SOIL REPORT.

REPORT BY:	ABH SOIL TESTING
JOB NUMBER:	10966
REPORT DATE:	31/10/18
SOIL CLASSIFICATION:	'P'

custovic DESIGN
H.I.A. MEMBER
REGISTERED
ARCHITECTURAL DRAFTING & DESIGN & BUILDING CONSULTANTS
First Floor 199-201 William Street, St.Albans
P: 9364 6336 M: 0418 379 902

NOTE TO OWNERS & BUILDERS

PLANS ARE TO BE CHECKED BY OWNERS/BUILDERS PRIOR TO CONSTRUCTION, INCLUDING DIMENSIONS, LEVELS, SITING, & ADJACENT HABITABLE ROOM WINDOWS ETC.

ANY DISCREPANCIES SHOULD BE FORWARDED TO THE RELEVANT BUILDING DESIGNER IMMEDIATELY.

OWNER/BUILDERS ARE TO CHECK & HAVE PLANS APPROVED BY DEVELOPERS PRIOR TO CONSTRUCTION AND ARE RESPONSIBLE TO NOTIFY DESIGNERS OF ANY COVENANTS OR RESTRICTIONS IF REQUIRED.

SITE CUTS & BATTERS SHALL NOT EXCEED A 45° SLOPE OR A 1:1 BATTER FOR CLAY & FOR SAND CUTS SHALL NOT EXCEED A 30° SLOPE OR ONE HORIZONTAL TO TWO VERTICAL BATTER

DP: DENOTES 100 x 50 COLORBOND DOWNPIPE
SPR: DENOTES SPREADER
RWH: RAIN WATER HEAD

CONNECTED STORMWATER DRAINAGE SYSTEM TO LEGAL POINT OF DISCHARGE VIA100mm DIAMETER P.V.C. SWD PIPE WITH 1:100 MIN FALL IN ACCORDANCE WITH LOCAL COUNCIL'S REGULATIONS & REQUIREMENTS

PROVIDE 100mm U.P.V.C. SWD PIPE WITH 1:100 MIN. FALL UNDER CONCRETE SLAB

FINISHED FLOOR LEVEL OF DWELLING SHALL BE 230mm MIN. ABOVE ADJACENT GROUND LEVEL & GROUND SURFACE SHALL BE GRADED AWAY FROM BUILDING

PROVIDE 1000 x 1000 MIN. SIZE LANDING WHERE FLOOR LEVEL IS GREATER THAN 190mm ABOVE ADJACENT GROUND LEVEL AT ALL ACCESS POINTS TO DWELLING

IT IS THE OWNERS RESPONSIBILITY TO OBTAIN APPROVAL FROM THE DEVELOPER FOR THE DRAWINGS SHOULD THEY BE REQUIRED. IT IS ALSO THE OWNERS RESPONSIBILITY TO ENSURE THAT THE PLANS DO NOT CONTRAVENE ANY COVENANTS

DO NOT RELY SOLELY ON THESE PLANS FOR UNDERGROUND ASSET LOCATIONS. THE BUILDER/CONTRACTOR IS TO PERFORM AN ONSITE INSPECTION FOR THE PRESENCE OF ANY ASSETS PRIOR TO THE COMMENCEMENT OF ANY WORKS ON SITE. SHOULD YOU REQUIRE AN ONSITE LOCATION, CONTACT THE RESPONSIBLE ASSET AUTHORITY DIRECTLY. CUSTOVIC DESIGN ENDORSES SAFE EXCAVATION AND ACCEPTS NO LIABILITY FOR ANY LOSS, DAMAGE OR INJURY BY ANY PERSON AS A RESULT OF ANY INACCURACY IN THESE PLANS OR UNSAFE EXCAVATION. PLEASE BE AWARE, THAT NOT ALL ASSETS MAY BE REPRESENTED ON THIS PLAN AND IT IS THE BUILDERS/CONTRACTORS RESPONSIBILITY TO IDENTIFY AND CONTACT THE RESPONSIBLE ASSET AUTHORITY FOR FURTHER INFORMATION

DIAL BEFORE YOU DIG
www.1100.com.au

1. THE BUILDER/ OWNER MUST CONTACT THIS OFFICE IMMEDIATELY. IF THE SITE CONDITIONS CHANGE IN ANY WAY COMPARED TO THE APPROVED ARCHITECTURAL PLANS/ ENGINEERING.
2. BRICK ARTICULATION JOINTS WHERE LOCATED AT OPENINGS MUST RUN CONTINOUSLY ALONG THE WINDOW AND DOOR FRAME IN ACCORDANCE WITH AS4773.2-2010.
3. IT IS THE BUILDERS RESPONSIBILITY TO ENSURE THAT THE SITING & FINSHED FFL FOR THE SLAB OF THE BUILDING IS IN ACCORDANCE WITH THE ENDORSED PLANS.
4. ALL MECHANICAL VENTILATION TO BE VENTED TO THE OUTSIDE AIR IN COMPLIANCE WITH THE NCC VOL2.
5. ALL SMOKE DETECTORS THROUGH OUT THE DWELLING MUST BE INTERCONNECTED WHERE THERE IS MORE THAN 1 SMOKE DETECTOR IN ACCORDANCE WITH PART 3.7.2 - NCC VOL 2 2014.
6. ALL EXPOSED EAVES ALONG THE BOUNDARY OR WITHIN 450MM OF THE BOUNDARY MUST ACHEIVE 60/60/60 IN ACCORDANCE WITH NCC AND MANUFACTURERS SPECS.

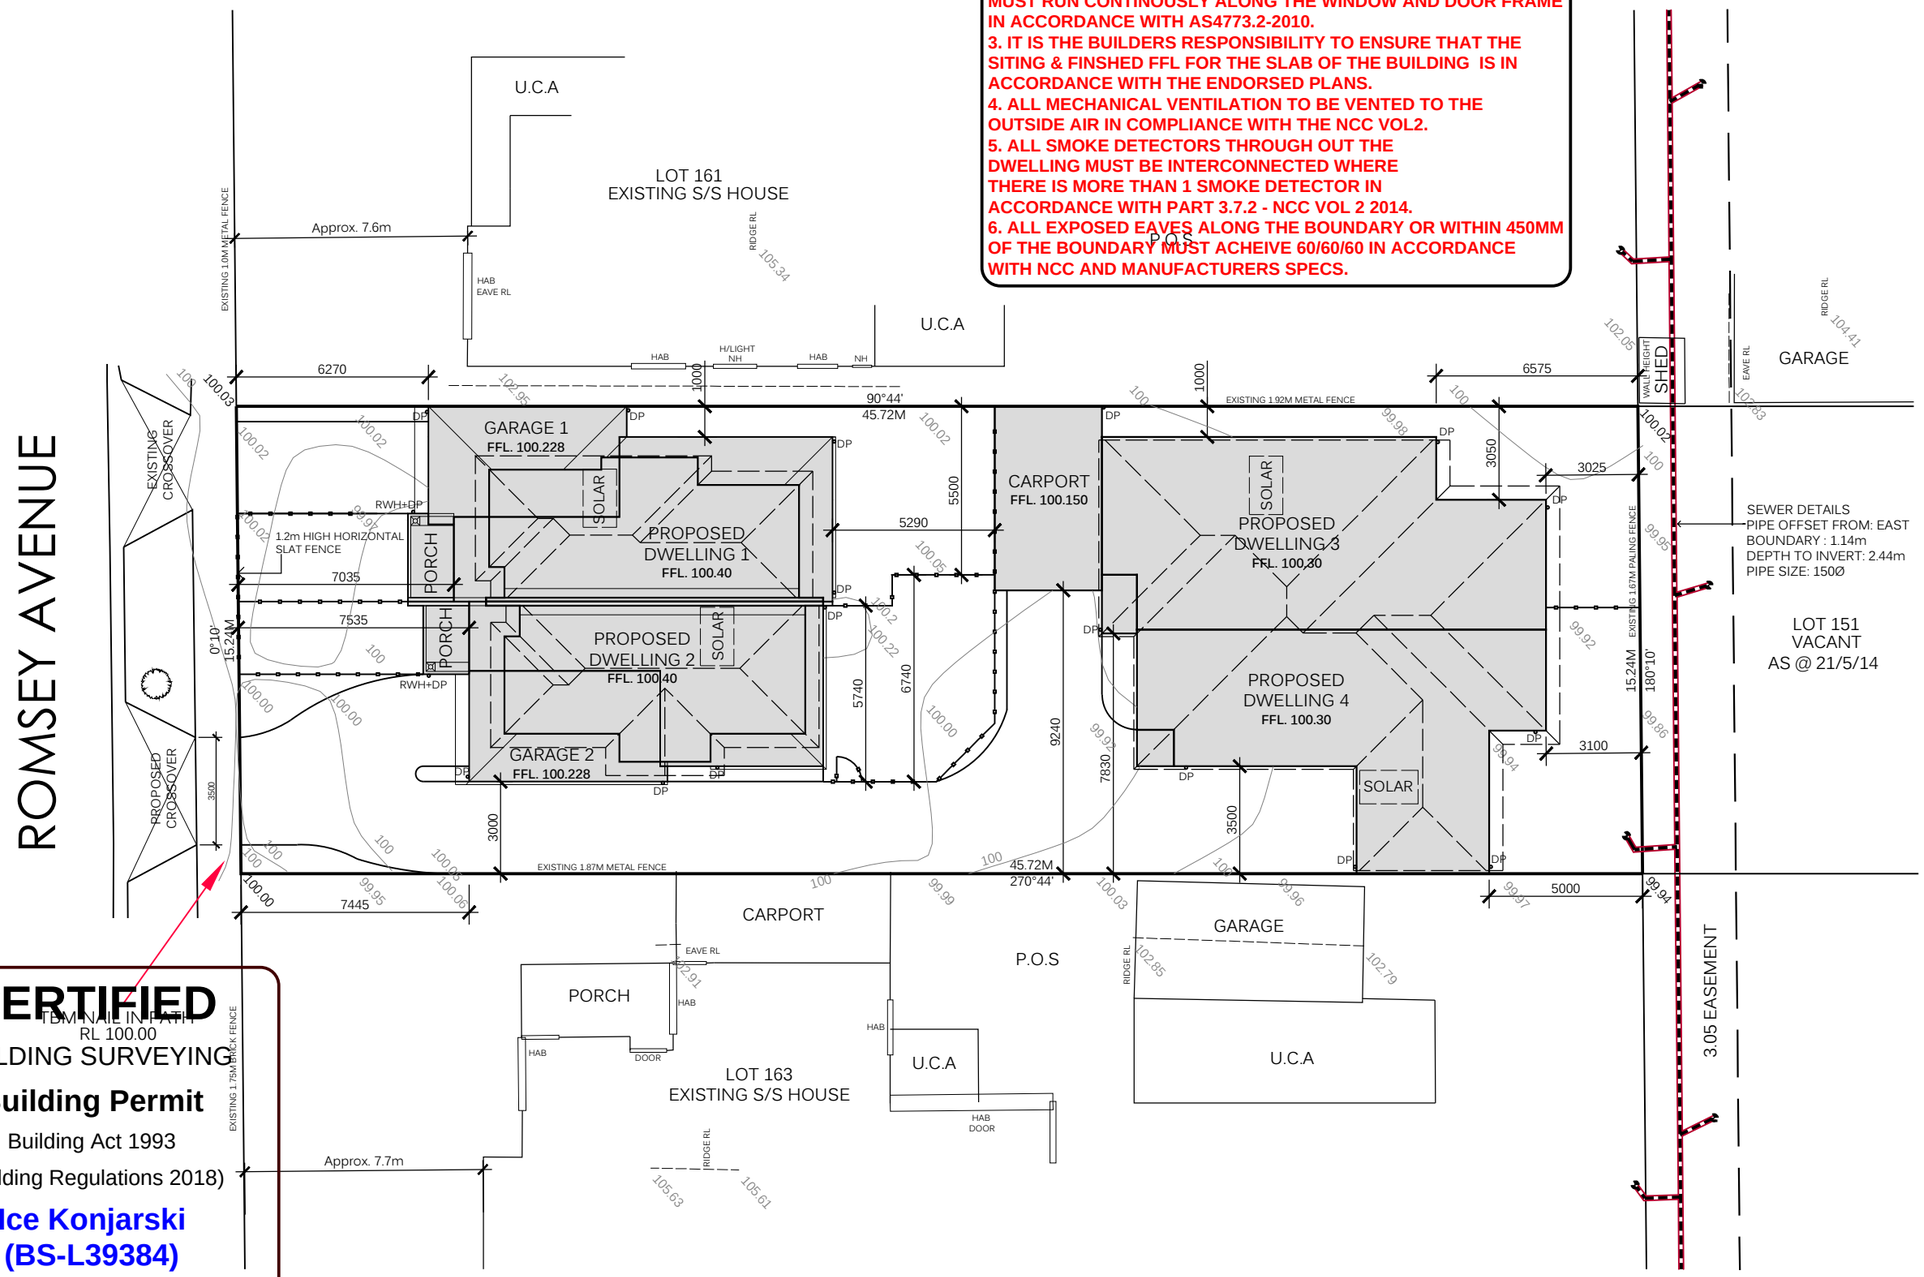

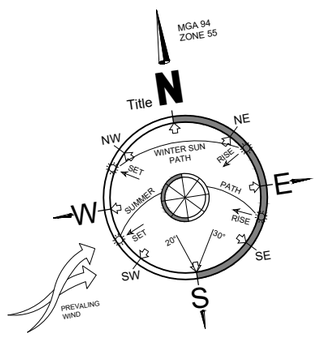

CERTIFIED
BUILDING SURVEYING
Building Permit
Building Act 1993
(Building Regulations 2018)
Ice Konjarski
(BS-L39384)
Date: 19 Aug 2019
BP: 7614151206228/0
INSPECTION BOOKINGS
9314 4888
24HRS NOTICE REQUIRED

SITE PLAN
SCALE 1:200

custovic DESIGN
H.I.A MEMBER
REGISTERED
ARCHITECTURAL DRAFTING & DESIGN & BUILDING CONSULTANTS
First Floor 199-201 William Street, St.Albans
P: 9364 6336 F: 9364 0330 M: 0418 379 902

PROPOSED: MULTI UNIT DEVELOPMENT
AT: LOT 28 ROMSEY AVENUE, SUNSHINE NORTH, VIC 3020
FOR: URAS ENTERPRISES

DO NOT SCALE DRAWINGS
ALL DIMENSIONS AND LEVELS TO BE CHECKED AND VERIFIED ON SITE BEFORE COMMENCING ANY WORK OR SHOP DRAWINGS.
THESE DESIGNS, PLANS AND SPECIFICATIONS AND THE COPYRIGHT THEREIN ARE THE PROPERTY OF CUSTOVIC DESIGN AND MUST NOT BE REPRODUCED OR COPIED WHOLLY OR IN PART WITHOUT THE WRITTEN PERMISSION OF CUSTOVIC DESIGN.

ISSUE: Preliminary	DATE:	DRAWING NAME:		JOB NUMBER:
rev_01: RFI	13/06/2019	SITE PLAN		14 040
rev_02:	SCALE:	SHEET NUMBER:		
rev_03:	1:200	02 OF 14		
rev_04:	SHEET SIZE:	DRAWN BY:	CHECKED BY:	
rev_05:	A3	M.D.	S.C.	